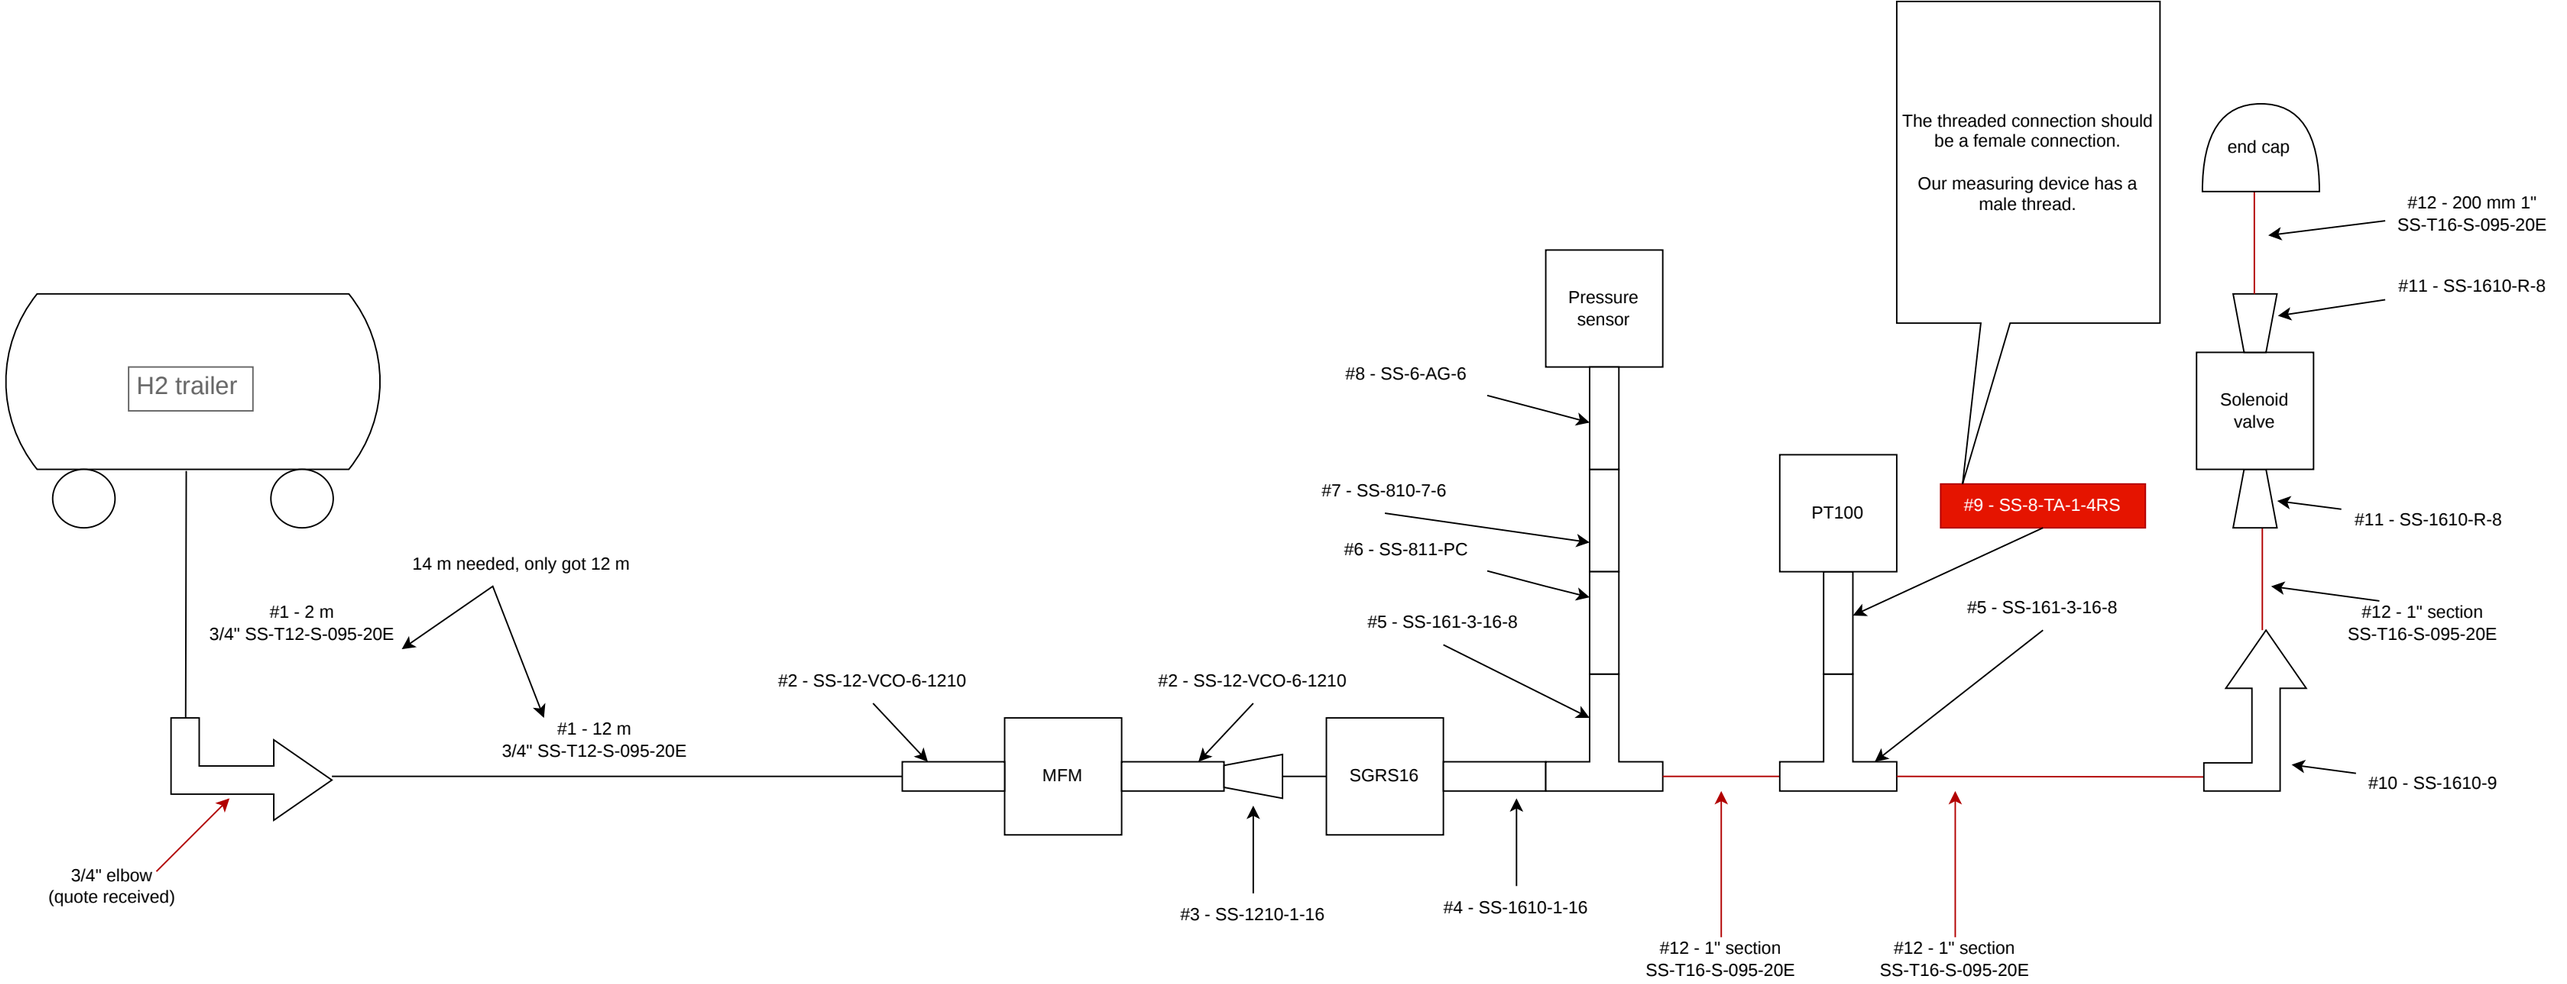
H2 trailer
14 m needed, only got 12 m
#1 - 2 m
3/4" SS-T12-S-095-20E
#1 - 12 m
3/4" SS-T12-S-095-20E
3/4" elbow
(quote received)
#2 - SS-12-VCO-6-1210
MFM
#2 - SS-12-VCO-6-1210
#3 - SS-1210-1-16
SGRS16
#4 - SS-1610-1-16
Pressure
sensor
#8 - SS-6-AG-6
#7 - SS-810-7-6
#6 - SS-811-PC
#5 - SS-161-3-16-8
The threaded connection should
be a female connection.
Our measuring device has a
male thread.
PT100
#9 - SS-8-TA-1-4RS
#5 - SS-161-3-16-8
#12 - 1" section
SS-T16-S-095-20E
#12 - 1" section
SS-T16-S-095-20E
end cap
#12 - 200 mm 1"
SS-T16-S-095-20E
#11 - SS-1610-R-8
Solenoid
valve
#11 - SS-1610-R-8
#12 - 1" section
SS-T16-S-095-20E
#10 - SS-1610-9

Text