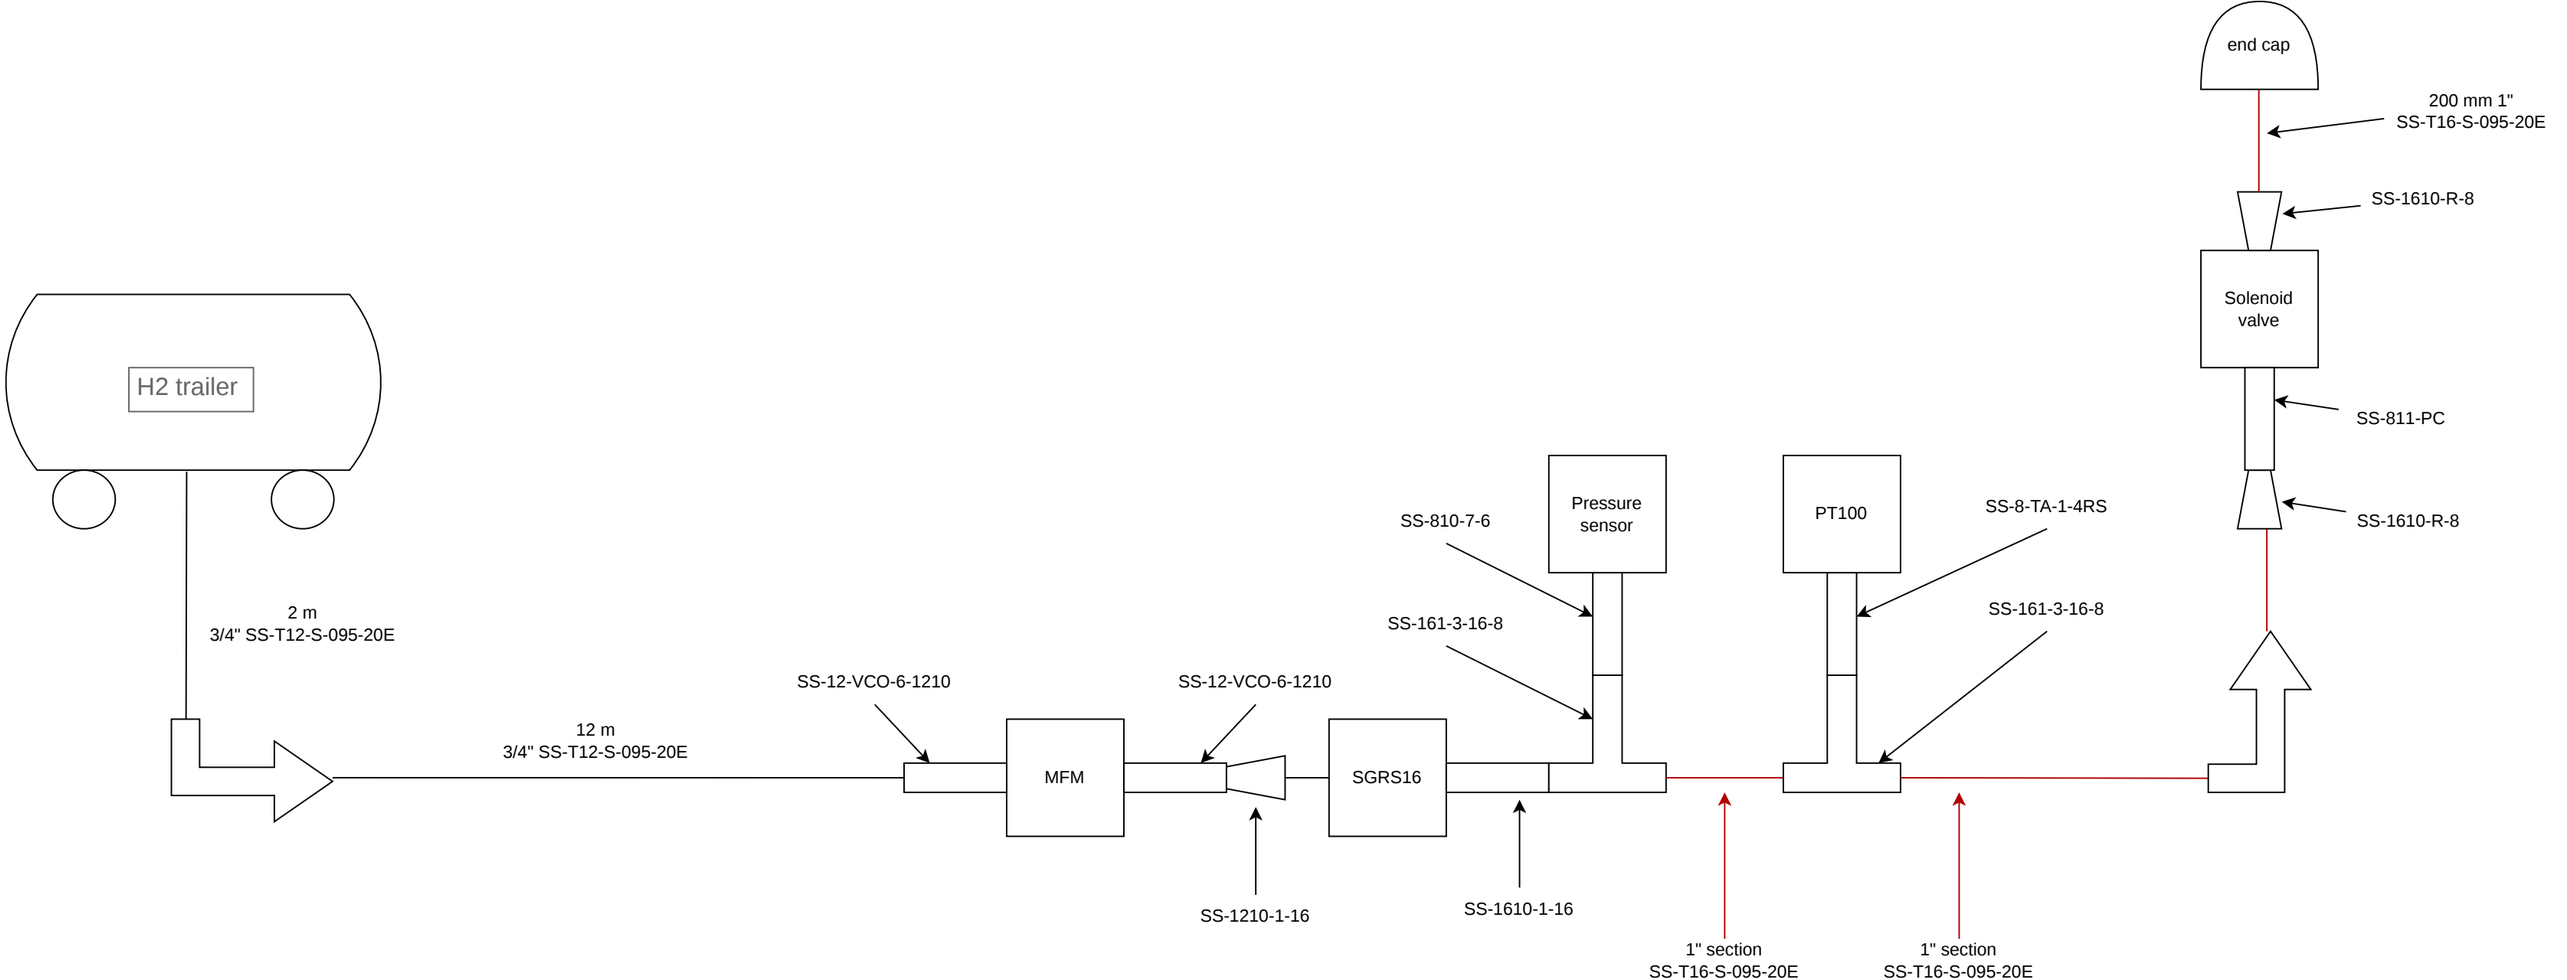
H2 trailer
2 m
3/4" SS-T12-S-095-20E
12 m
3/4" SS-T12-S-095-20E
SS-12-VCO-6-1210
MFM
SS-12-VCO-6-1210
SS-1210-1-16
SGRS16
SS-810-7-6
SS-161-3-16-8
Pressure sensor
SS-1610-1-16
PT100
SS-8-TA-1-4RS
SS-161-3-16-8
1" section
SS-T16-S-095-20E
1" section
SS-T16-S-095-20E
end cap
200 mm 1"
SS-T16-S-095-20E
SS-1610-R-8
Solenoid valve
SS-811-PC
SS-1610-R-8